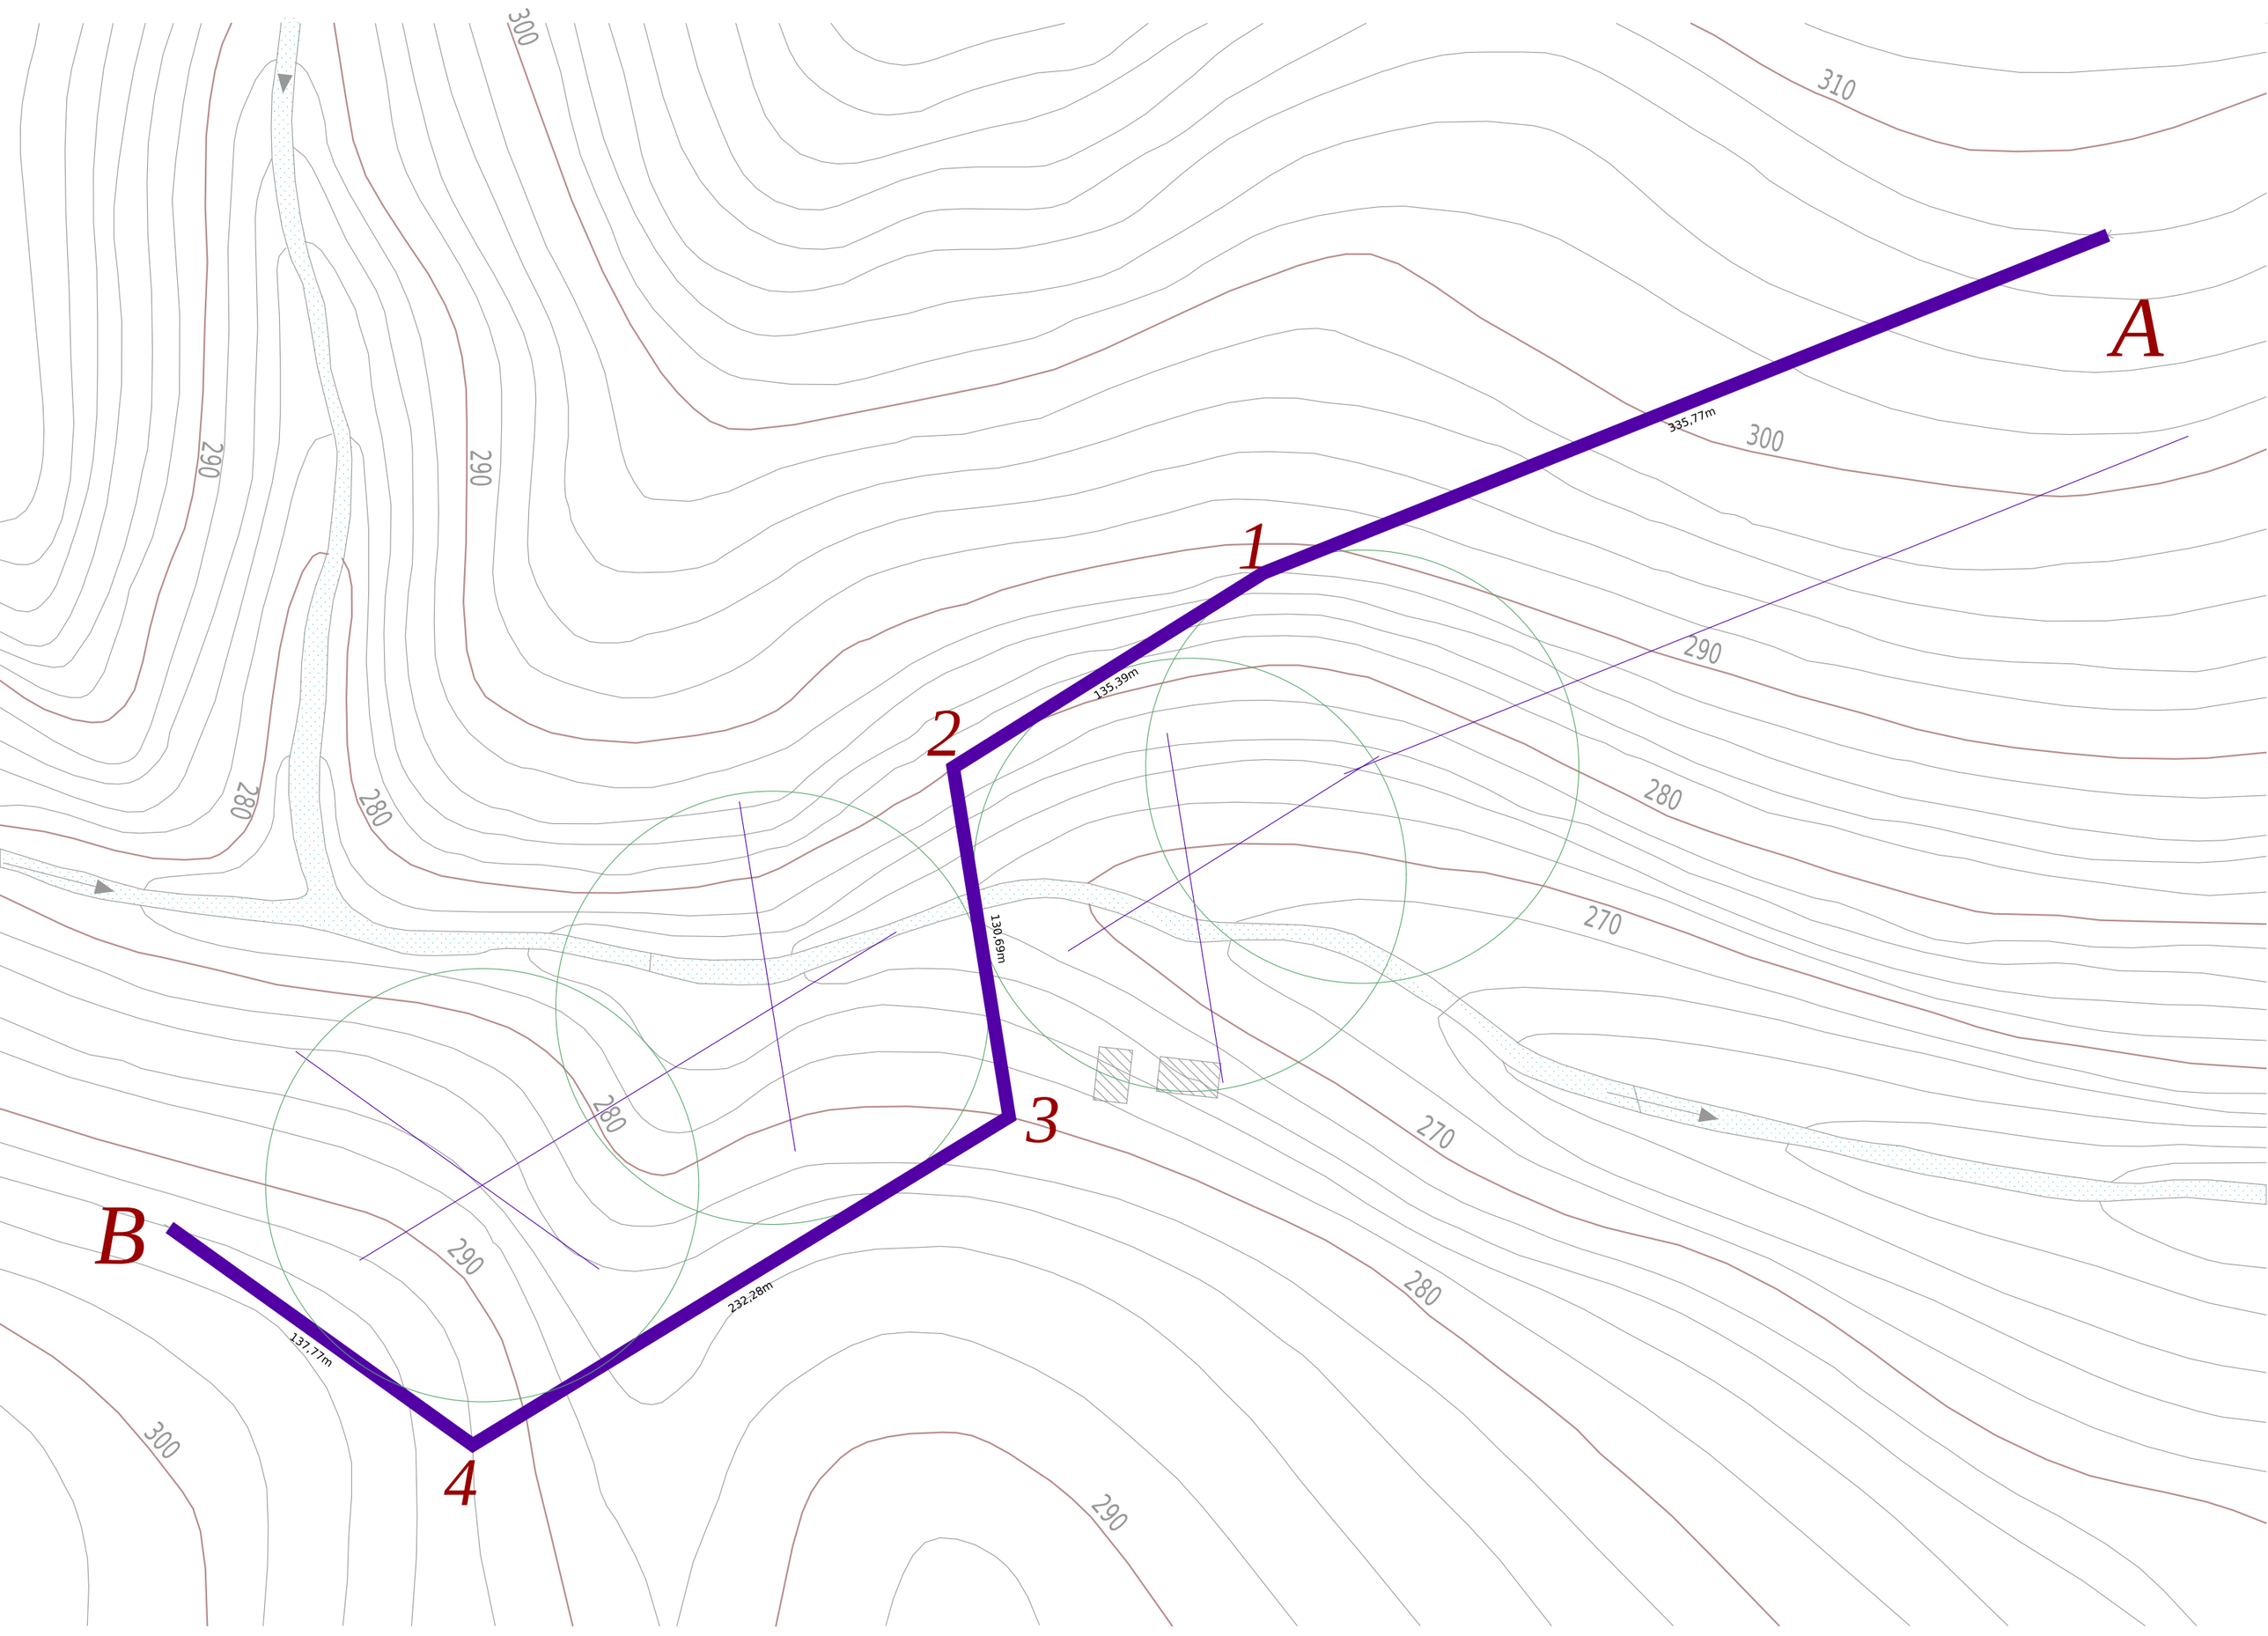

A
1
2
3
4
B
335,77m
135,39m
130,69m
232,28m
137,77m
310
300
290
280
270