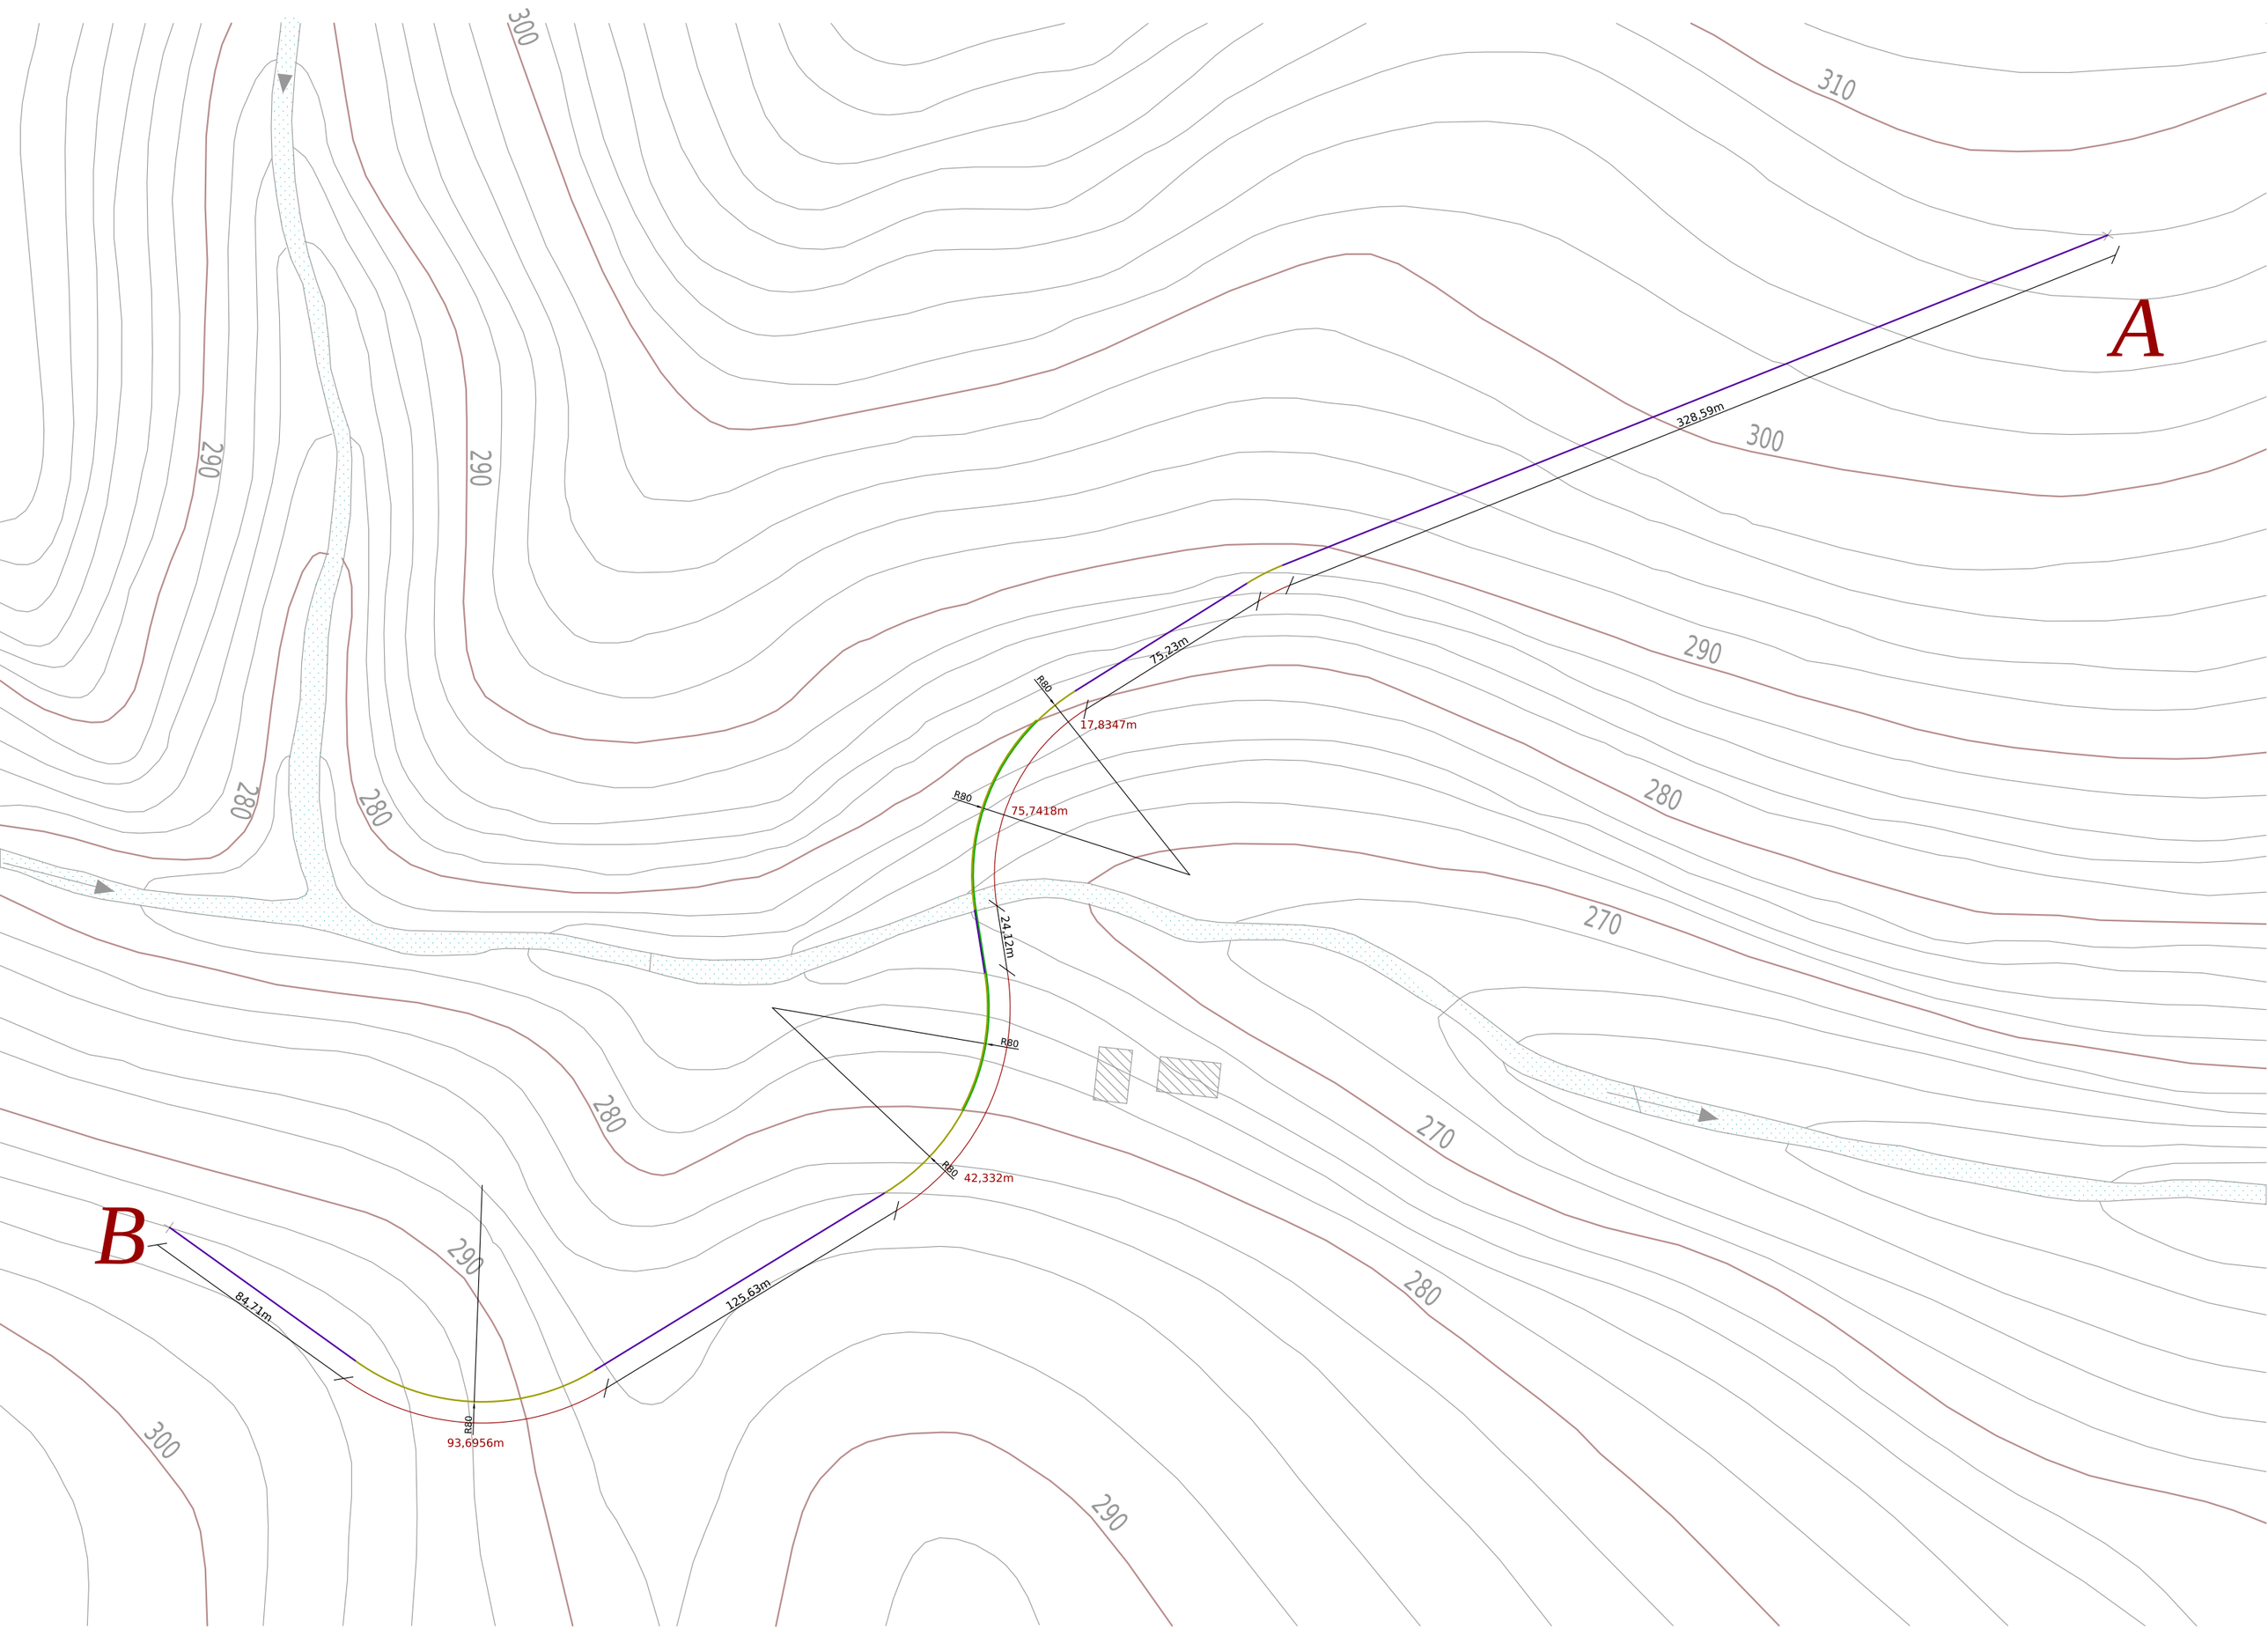

A
328,59m
75,23m
R80
17,8347m
R80
75,7418m
24,12m
R80
R80
42,332m
B
84,71m
125,63m
R80
93,6956m
310
300
290
280
270